


F-2 FACHADA POSTERIOR (OESTE)

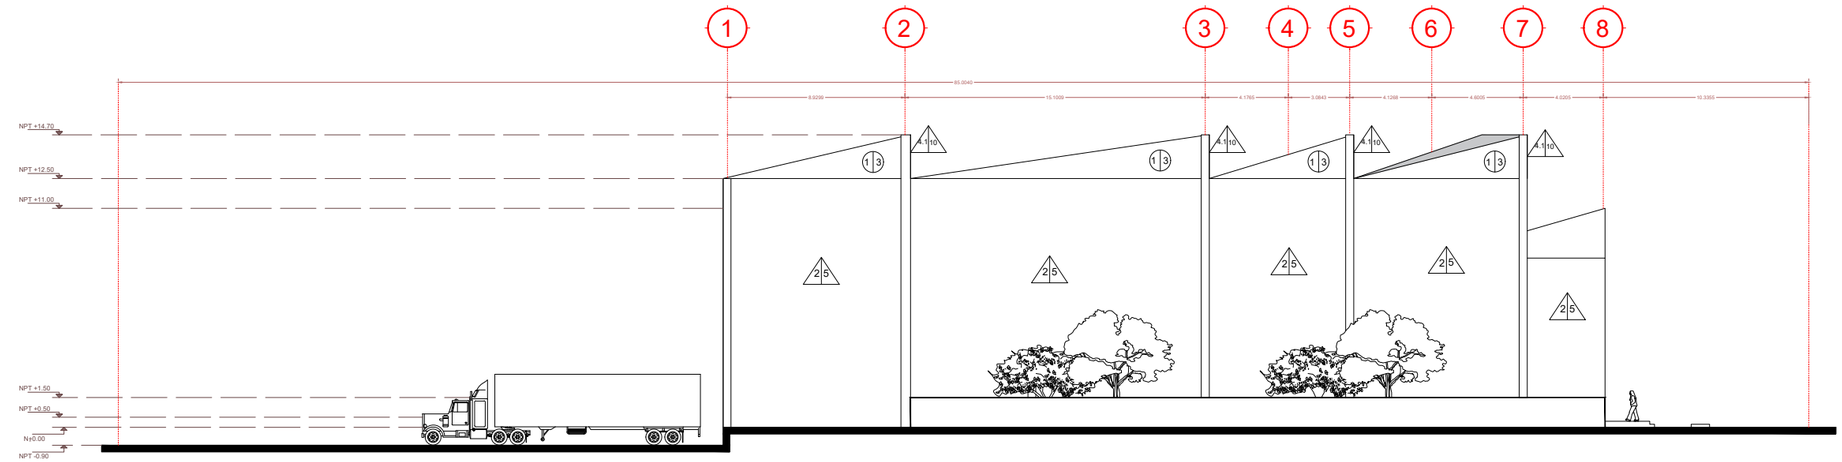

F-4 FACHADA LATERAL (SUR)

A|B MUROS

No.	ACABADO BASE
1	MURO PARA FACHADA DE CONCRETO F'C=250 KG/CM2 DE 18 CM DE ESPESOR TERMINADO APARENTE, CON ACERO DE REFUERZO DE FY = 4200 KG/CM2 DE ACUERDO CON EL CÁLCULO ESTRUCTURAL.
2	MURO DE BLOCK HUECO 12X20X40 CM, ASENTADO CON MORTERO A PROPORCIÓN 1:2:6 CEMENTO-CAL-ARENA, JUNTAS A 1 CM
3	BASE NO MENOR A 3CMS DE MORTERO FONCERBOND 400 MARCA FONCER EN SU PARTE INFERIOR DEL MURO, CON ANCLA PARA INSTALACIÓN DE VITROBLOCK 1 X 4 X 40.6 CMS MARCA FONCER, DOBLADO Y FIJADO AL MURO
4	MURO DE PANEL DE YESO FIRE REY DE 5/8" DE ESPESOR PARA RECIBIR PUERTA CORREDIZA QUE SE OCULTARÁ EN MEDIO DEL MURO, CAPA UNIFORME DE 2MM DE REDIMIX EN TODA LA SUPERFICIE,JUNTAS ENTRE PLACAS CUBIERTAS CON CINTA DE REFUERZO Y COMPUERTO PARA JUNTAS
4.1	COLUMNA HSS 16 X 0.5

A|B MUROS

No.	ACABADO FINAL
5	APLANADO DE MORTERO PROPORCIÓN 1:3 CEMENTO-ARENA FINA CERNIDA, DESPUÉS APLICAR SOBRE SUPERFICIE HÚMEDA A UNA SOLA MANO CHUKRET EN COLOR BLANCO I-010 ACABADO SEMIMATE MARCA COMEX, PREVIAMENTE SELLADO CON SELLADOR PRACTIKO 3 EN 1 MARCA COMEX
6	APLANADO DE MORTERO PROPORCIÓN 1:3 CEMENTO-ARENA FINA CERNIDA, DESPUÉS APLICAR SOBRE SUPERFICIE SUPERFICIALMENTE HÚMEDA A UNA SOLA MANO CHUKRET EN COLOR LORCA I5-09 ACABADO SEMIMATE MARCA COMEX
7	APLANADO DE YESO PROPORCIÓN 0.5:1 AGUA-YESO, DESPUÉS APLICAR SOBRE SUPERFICIE HÚMEDA A UNA SOLA MANO CHUKRET EN COLOR ASTURIAS M4-06 ACABADO SEMIMATE MARCA COMEX, PREVIAMENTE SELLADO CON SELLADOR PRACTIKO 3 EN 1 MARCA COMEX
8	VITROBLOCK DE TRAMA DIAMANTE 19X19X8 CMS COLOCADOS CON SEPARACIONES DE 5MM, UNIDOS CON MORTERO FORCERBOND 400 MARCA FORCE BIEN APISONADO Y DISTRIBUIDO, REFORZADO CON ESCALERILLA INDEX INTERNACIONAL
9	MURO DE CELOSÍA DE BARRO C9 MARCA TALAMSA DE 15 X 15 X 8 CM
10	CAPA DISTRIBUIDA Y LIGERA DE ESMALTE ANTICORROSIVO RUST OLEUM METAL PROTECTION

A|B PISOS

No.	ACABADO BASE
1	FIRME DE CONCRETO ARMADO TERMINADO NIVELADO Y PULIDO PARA RECIBIR ACABADO.
2	CAPA DE 5 CM DE TIERRA VEGETAL
3	SISTEMA LOSACERO CALIBRE 22, CON MALLA ELECTROSOLDADA 6X6 Y PERNOS DE CORTANTE SOBRE VIGAS SECUNDARIAS, CON UNA CAPA DE CONCRETO F'C=250 KG/CM2 DE 5 CM DE GROSOR
No.	ACABADO FINAL
4	APLICAR SOBRE SUPERFICIE HÚMEDA A UNA SOLA MANO CHUKRET EN COLOR LORCA I5-09 ACABADO SEMIMATE MARCA COMEX, PREVIAMENTE SELLADO CON SELLADOR PRACTIKO 3 EN 1 MARCA COMEX
5	VEGETACIÓN INDICADA EN PLANO
6	ACABADO CONCRETO PULIDO

A|B PLAFÓN

No.	ACABADO BASE
1	LOSA DE CONCRETO F'C=250 KG/CM2 DE 12 CM DE ESPESOR TERMINADO APARENTE, CON ACERO DE REFUERZO DE FY = 4200 KG/CM2 DE ACUERDO CON EL CÁLCULO ESTRUCTURAL
2	LOSA DE CONCRETO F'C=250 KG/CM2 DE # CM DE ESPESOR TERMINADO APARENTE, CON ACERO DE REFUERZO F'Y=4200 KG/CM2 Y MALLA ELECTROSOLDADA 6X6 DE ACUERDO CON EL CÁLCULO ESTRUCTURAL.
No.	ACABADO FINAL
3	EN SUPERFICIE HÚMEDA APLICAR CHUKRET EN COLOR ASTURIAS M4-06 ACABADO SEMIMATE MARCA COMEX, PREVIAMENTE SELLADO CON SELLADOR PRACTIKO 3 EN 1 MARCA COMEX A UNA MANO, IMPERMEABILIZADO CON IMPERMEBAILIZANTE FESTER ACRITON PROSHIELD MAX 12 AÑOS EN COLOR BLANCO MARCA FESTER

NOMBRE DEL PROYECTO:
NAVE INDUSTRIAL

TIPO DE TRAMITE:
OBRA NUEVA

DATOS DEL PROPIETARIO
KARLA JANET GONZÁLEZ RIVERA

FIRMA:

- DECLARO QUE LOS DATOS CONSIGNADOS EN ESTE PLANO SON VERIDICOS.

DATOS DEL PREDIO
AREA: 5,962.66 m2
DIRECCIÓN
AV. 16 DE SEPTIEMBRE, COYOTILLOS C.P.: 76245
MUNICIPIO EL MARQUÉS, QRO.

USO
HABITACIONAL ☐
SERVICIOS ☐
COMERCIAL ☐
INDUSTRIAL ☒

DATOS DEL D.R.O
NOMBRE:
ING. ARQ. JESÚS ALFREDO QUEZADA GARCÍA
CEDULA PROFESIONAL:
1408221
FIRMA:

NOTAS RELEVANTES:
Cualquier modificación, alteración u omisión respecto a lo indicado en los planos, detalles y especificaciones del proyecto deberá contar con autorización previa y por escrito del proyectista.
Cualquier cambio ejecutado sin dicha aprobación invalida el alcance técnico del proyecto, por lo que no se garantiza la seguridad, funcionamiento, viabilidad ni cumplimiento normativo de los elementos arquitectónicos, acabados, instalaciones, cancelería y demás componentes.
El proyectista no asume responsabilidad por daños o consecuencias derivados de modificaciones no autorizadas.


PLANO 22/50

- COMO DIRECTOR RESPONSABLE DE OBRA DECLARO QUE LOS DATOS CONTENIDOS EN ESTE PLANO SON VERÍDICOS.
- COMO DIRECTOR RESPONSABLE DE OBRA DECLARO QUE ESTE PLANO HA SIDO ELABORADO DE ACUERDO AL REGLAMENTO DE CONSTRUCCIÓN PARA EL MUNICIPIO DE EL MARQUÉS, QRO., CÓDIGO URBANO DEL ESTADO DE QUERÉTARO Y DEMAS LEGISLACIÓN VIGENTE APLICABLE.

DATOS DE LA CONSTRUCCION

CONCEPTO	A CONSTRUIR OBRA NUEVA O AMPLIACION	CONSTRUIDA SIN LICENCIA, A REGULARIZAR	AUTORIZADO CON LICENCIA(S) ANTERIOR(ES) M2 Y TERMINACIÓN DE OBRA FOLIOS:	
SOTANO	2,432.47			
PLANTA BAJA	5,049.13			
PRIMER NIVEL				
SEGUNDO NIVEL				
TERCER NIVEL				
MEZZANINE	1,583.86			
* NIVEL				
* NIVEL				
TOTAL M2 TECHADOS	9,065.46			
PASILLO (PISO)	278.65			
PATIO (PISO)				
ESTACIONAM. (PISO)	532.84			
TOT. M2 CONST. S/TECHAR	811.49			
JARDIN (área sin construcción)	628.98			
BARDEO ML	75.27			
ALINEAMIENTO ML				

SIMBOLOGÍA:
NIVEL DE PISO TERMINADO NPT +0.15
NIVEL N±0.00
NIVEL DE TECHO TERMINADO NTT +14.70
ACABADOS EN MUROS A|B
ACABADOS EN PISOS A|B

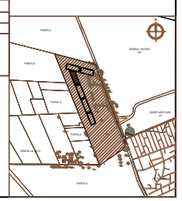

CONTENIDO DEL PLANO:
ACABADOS EN FACHADAS:
SUR Y OESTE

ESCALA: 1:300

COTAS:
METROS

CLAVE:
AC-06

PLANOS COMPLEMENTARIOS: