

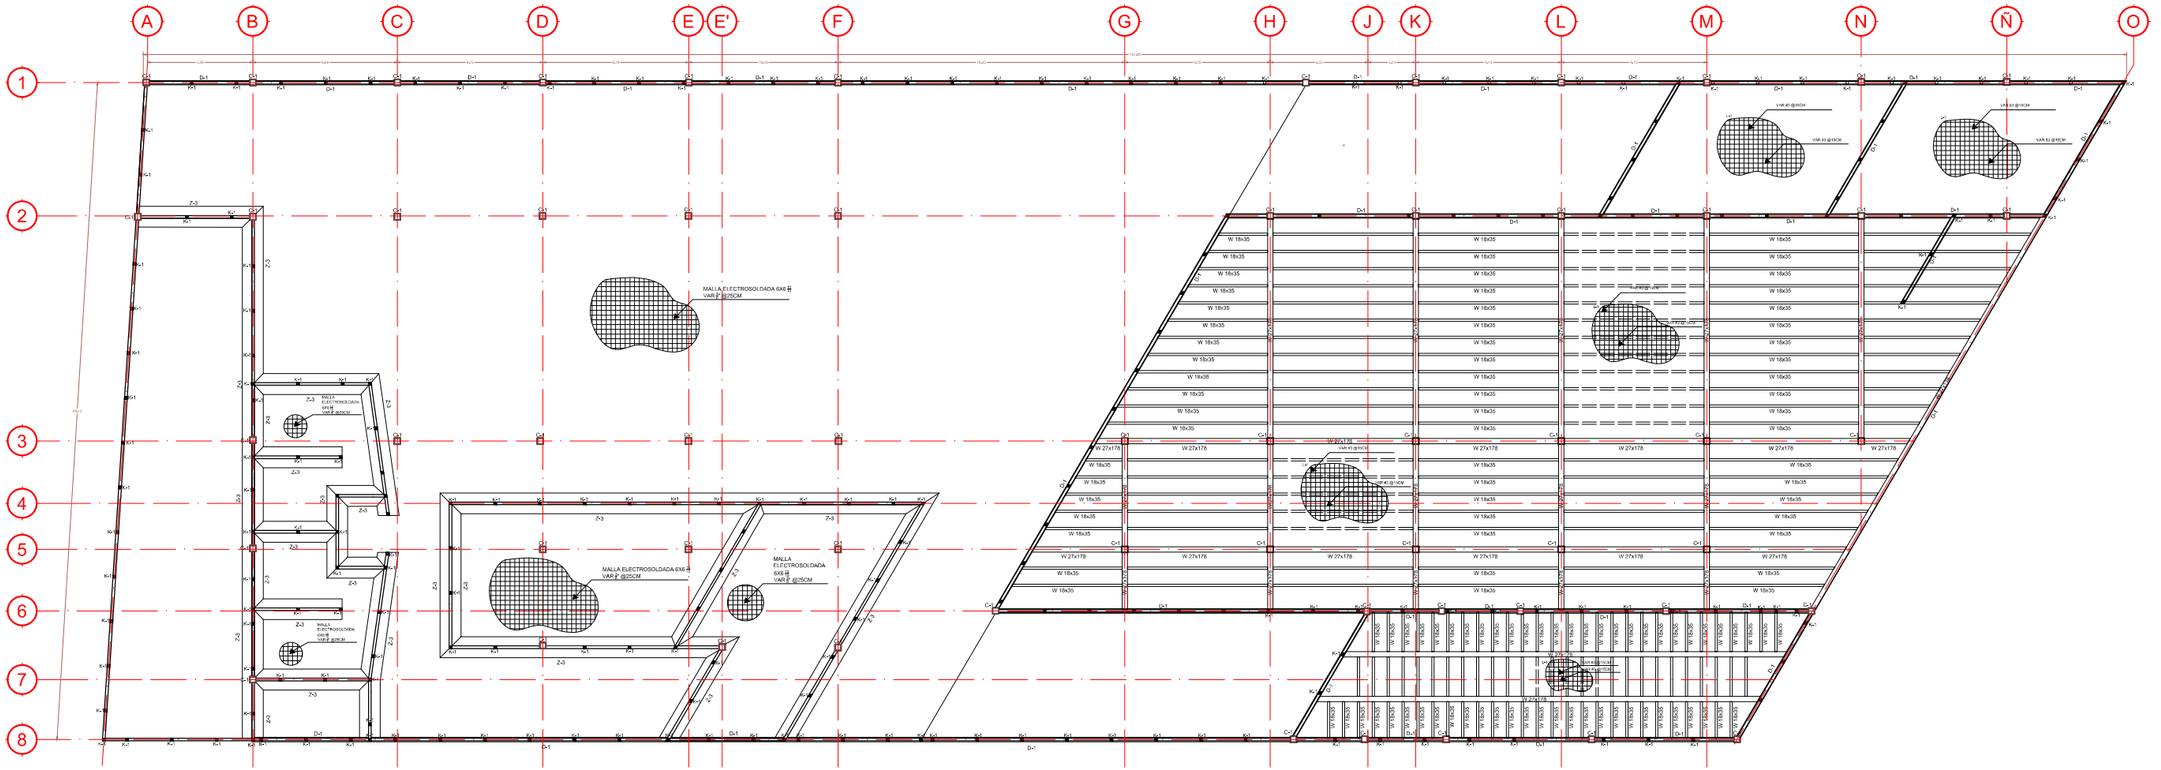


PLANTA BAJA
ZAPATAS, CASTILLOS Y FIRME


PLANTA BAJA
DISTRIBUCIÓN DE VIGAS Y ARMADO DE LOSA

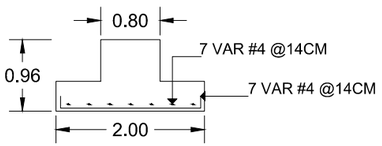

Z-1

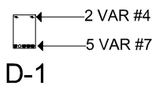


D-1

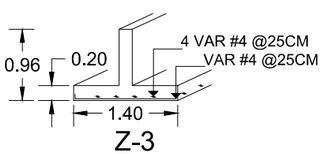


Z-3




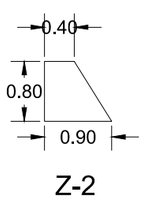


Z-2

Detalle armado L-1

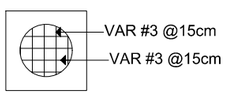

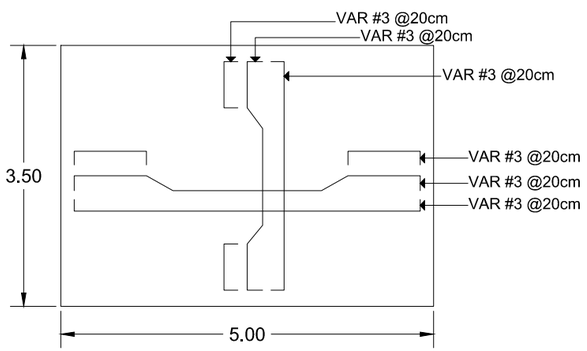

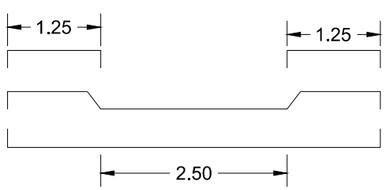

NOMBRE DEL PROYECTO:
NAVE INDUSTRIAL

TIPO DE TRAMITE:
OBRA NUEVA

DATOS DEL PROPIETARIO
KARLA JANET GONZÁLEZ RIVERA

FIRMA:

- DECLARO QUE LOS DATOS CONSIGNADOS EN ESTE PLANO SON VERIDICOS.

DATOS DEL PREDIO
AREA: 5,962.66 m2
DIRECCIÓN
AV. 16 DE SEPTIEMBRE, COYOTILLOS C.P.: 76245
MUNICIPIO EL MARQUÉS, QRO.

USO
HABITACIONAL ☐
SERVICIOS ☐
COMERCIAL ☐
INDUSTRIAL ☒

DATOS DEL D.R.O
NOMBRE:
ING. ARQ. JESÚS ALFREDO QUEZADA GARCÍA
CEDULA PROFESIONAL:
1408221
FIRMA:

NOTAS RELEVANTES:
Cualquier modificación, alteración u omisión respecto a lo indicado en los planos, detalles y especificaciones del proyecto deberá contar con autorización previa y por escrito del proyectista.
Cualquier cambio ejecutado sin dicha aprobación invalida el alcance técnico del proyecto, por lo que no se garantiza la seguridad, funcionamiento, viabilidad ni cumplimiento normativo de los elementos arquitectónicos, acabados, instalaciones, cancelería y demás componentes.
El proyectista no asume responsabilidad por daños o consecuencias derivados de modificaciones no autorizadas.

PLANO 40/50

- COMO DIRECTOR RESPONSABLE DE OBRA DECLARO QUE LOS DATOS CONTENIDOS EN ESTE PLANO SON VERIDICOS.
- COMO DIRECTOR RESPONSABLE DE OBRA DECLARO QUE ESTE PLANO HA SIDO ELABORADO DE ACUERDO AL REGLAMENTO DE CONSTRUCCIÓN PARA EL MUNICIPIO DE EL MARQUÉS, QRO., CÓDIGO URBANO DEL ESTADO DE QUERÉTARO Y DEMÁS LEGISLACIÓN VIGENTE APLICABLE.

DATOS DE LA CONSTRUCCIÓN

CONCEPTO	A CONSTRUIR OBRA NUEVA O AMPLIACION	CONSTRUIDA SIN LICENCIA, A REGULARIZAR	AUTORIZADO CON LICENCIA(S) ANTERIOR(ES) M2 Y TERMINACIÓN DE OBRA FOLIOS:		
SOTANO	2,432.47				
PLANTA BAJA	5,049.13				
PRIMER NIVEL					
SEGUNDO NIVEL					
TERCER NIVEL					
MEZZANINE	1,583.86				
* NIVEL					
* NIVEL					
TOTAL M2 TECHADOS	9,065.46				
PASILLO (PISO)	278.65				
PATIO (PISO)					
ESTACIONAM. (PISO)	532.84				
TOT. M2 CONST. S/TECHAR	811.49				
JARDIN (área sin construcción)	628.98				
BARDEO ML	75.27				
ALINEAMIENTO ML					

SIMBOLOGÍA:
COLUMNA C-1
ZAPATA Z-1
CASTILLO K-1
CADENA DE CIMENTACIÓN D-1
ARMADO DE LOSA
VIGA W 27x178

CONTENIDO DEL PLANO:
PLANTA BAJA: ESTRUCTURAL

ESCALA: 1:400

COTAS: METROS

CLAVE: EST-04/05

PLANOS COMPLEMENTARIOS:

